


ЭКСПЛИКАЦИЯ ЗДАНИЙ И СООРУЖЕНИЙ

Номер по плану	Наименование	Примечание
1	Многоэтажный жилой дом 5-15 этажей 6-и секционный	Проектируемый
2	Многоэтажный жилой дом 5-15 этажей 6-и секционный	Проектируемый
3	Многоэтажный жилой дом 5-15 этажей 6-и секционный	Существующий
4	Многоэтажный жилой дом 7-13 этажей 3-х секционный	Ранее запроектированный
5	Многоэтажный жилой дом 5-15 этажей 6-и секционный	Ранее запроектированный

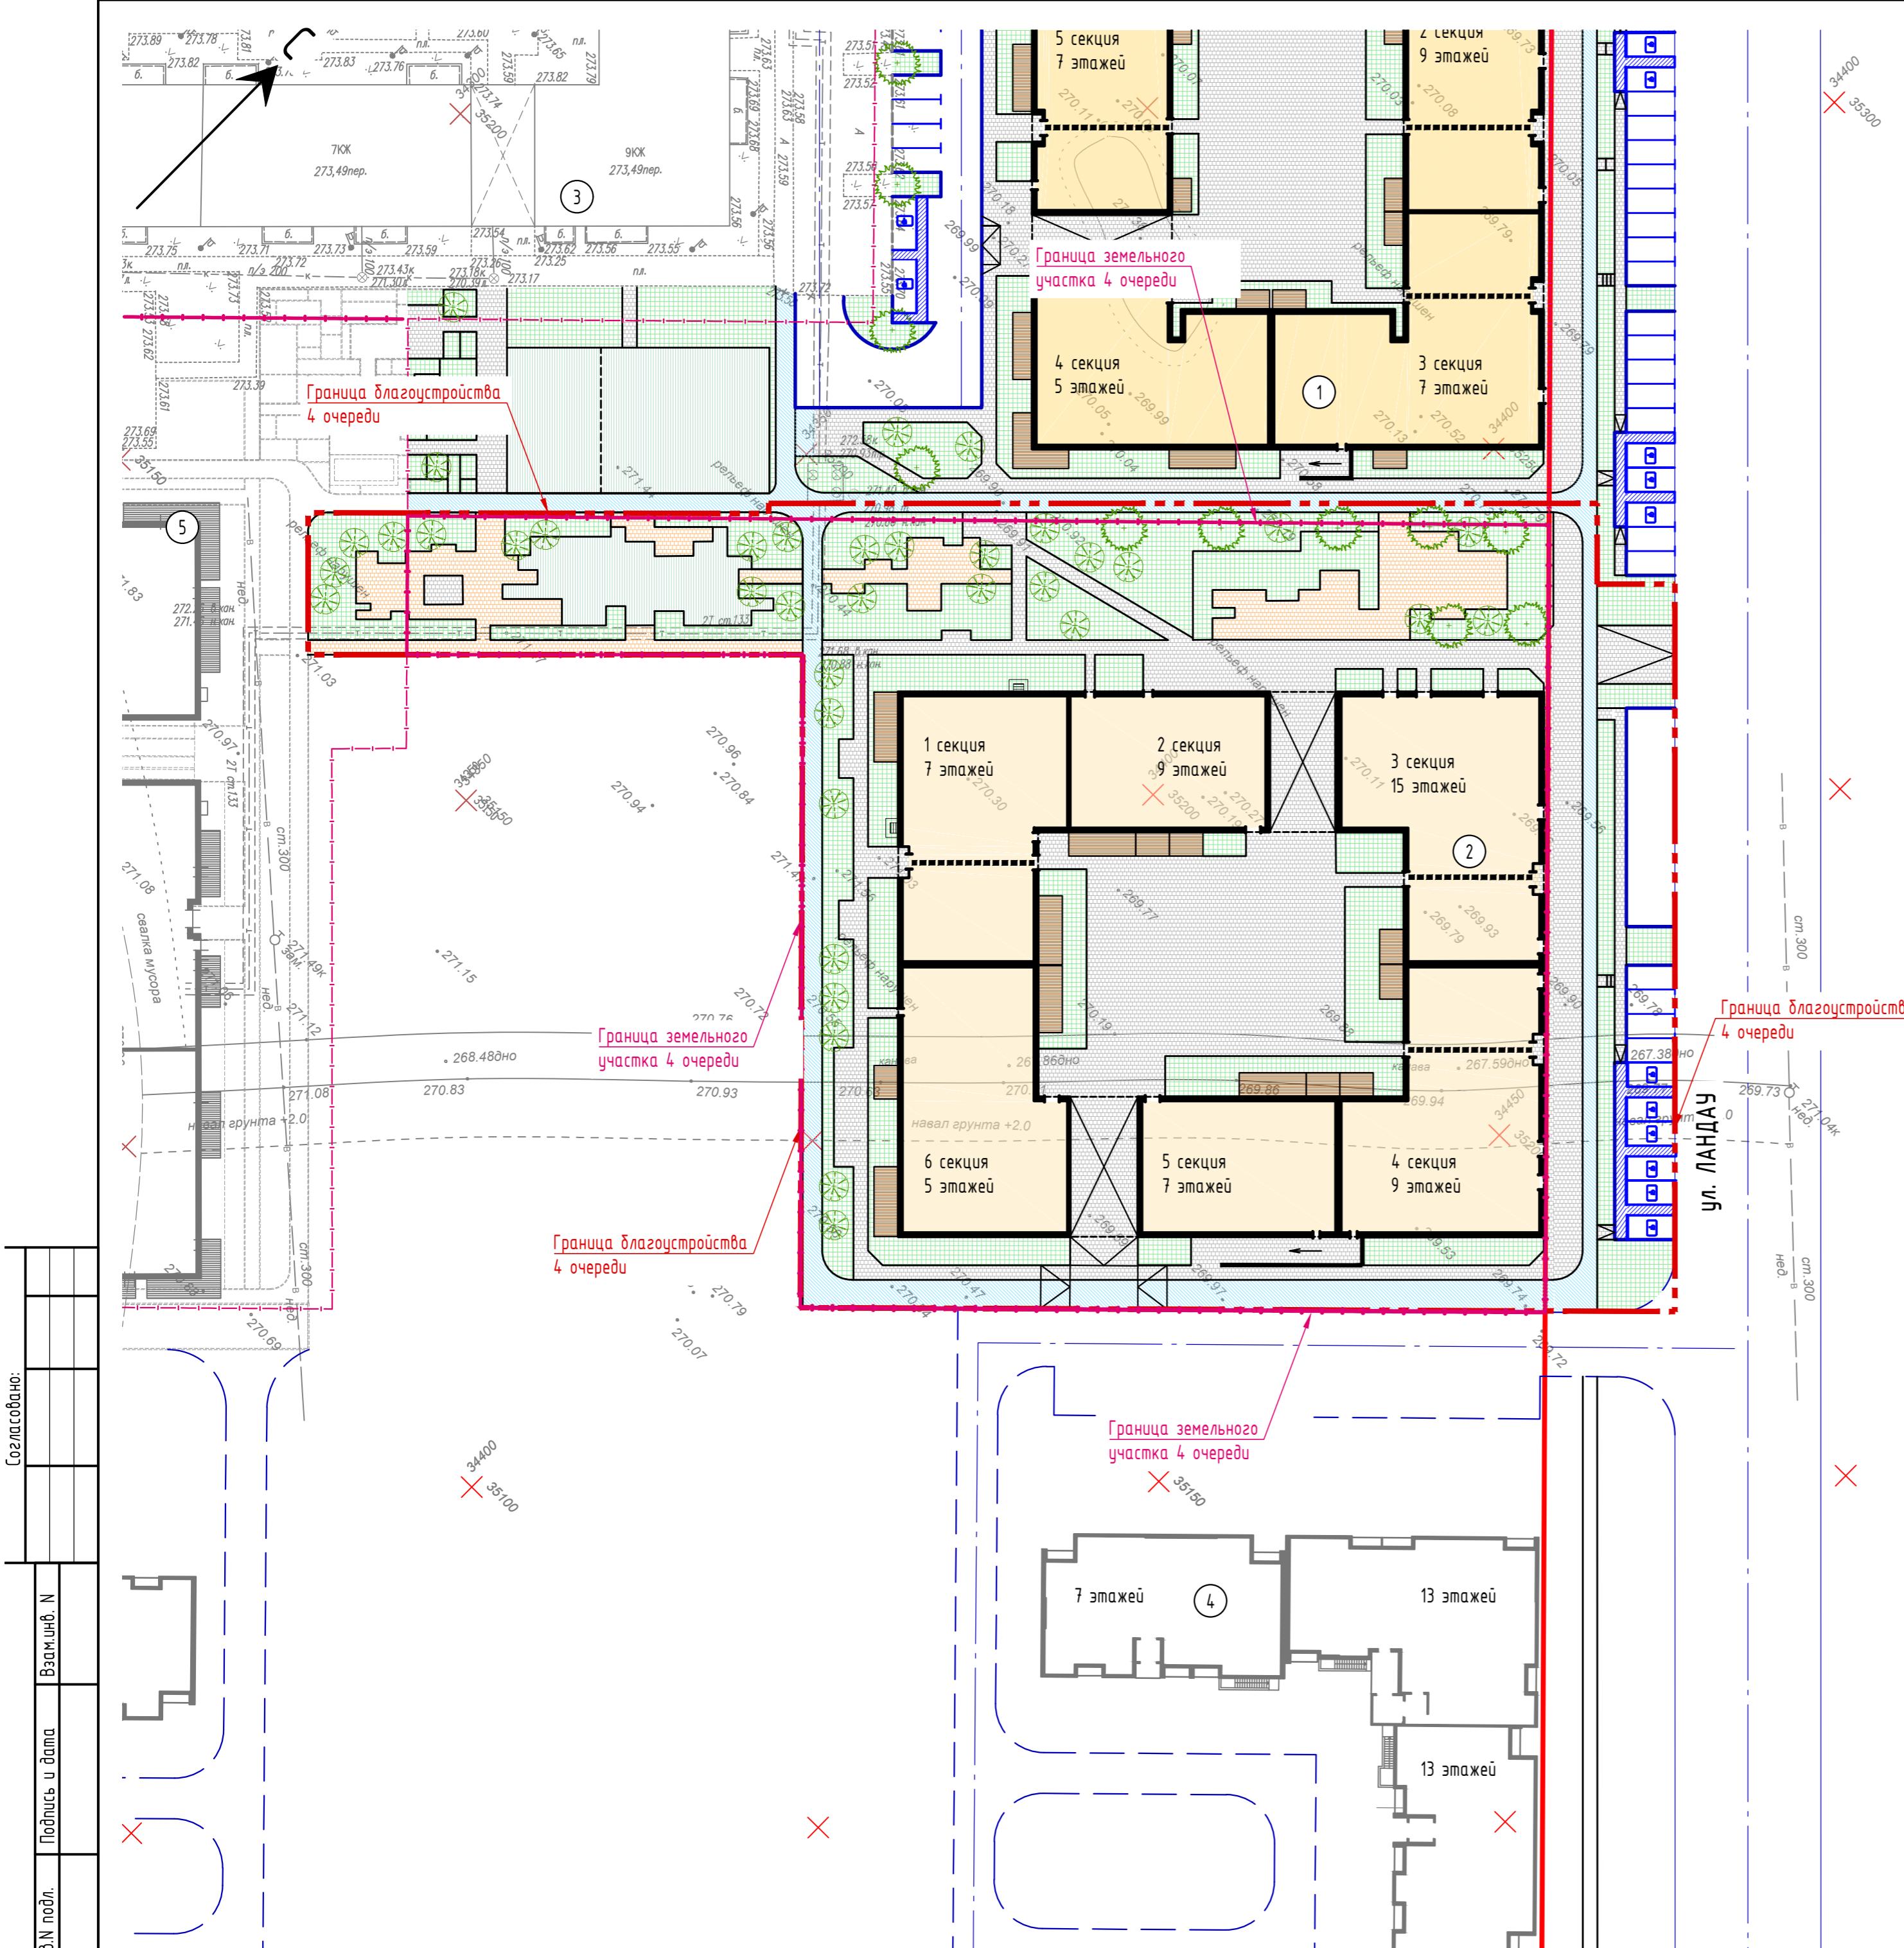

44-17-04-ПЗУ

Жилая застройка в границах улиц Суходольская - Ландau - Ручейная в Верх-Исетском районе г. Екатеринбурга. 4 очередь строительства комплекса жилых домов с встроенным нежилыми помещениями

1	-	Зам.	13-18	Рисунок	02.18	Схема планировочной организации земельного участка	Стадия	Лист	Листов
Изм. Кол. ч		Лист № листок		Подпись	Дата				
Разработал	Рябих				12.17				
Проверил	Бабкин				12.17				
Н.Контроль	Прибалова				12.17				
ГИП	Бабкин				12.17	Схема планировочной организации земельного участка	П	2	-

000
"Строительное
Проектирование "КУБ"
CUBE

