


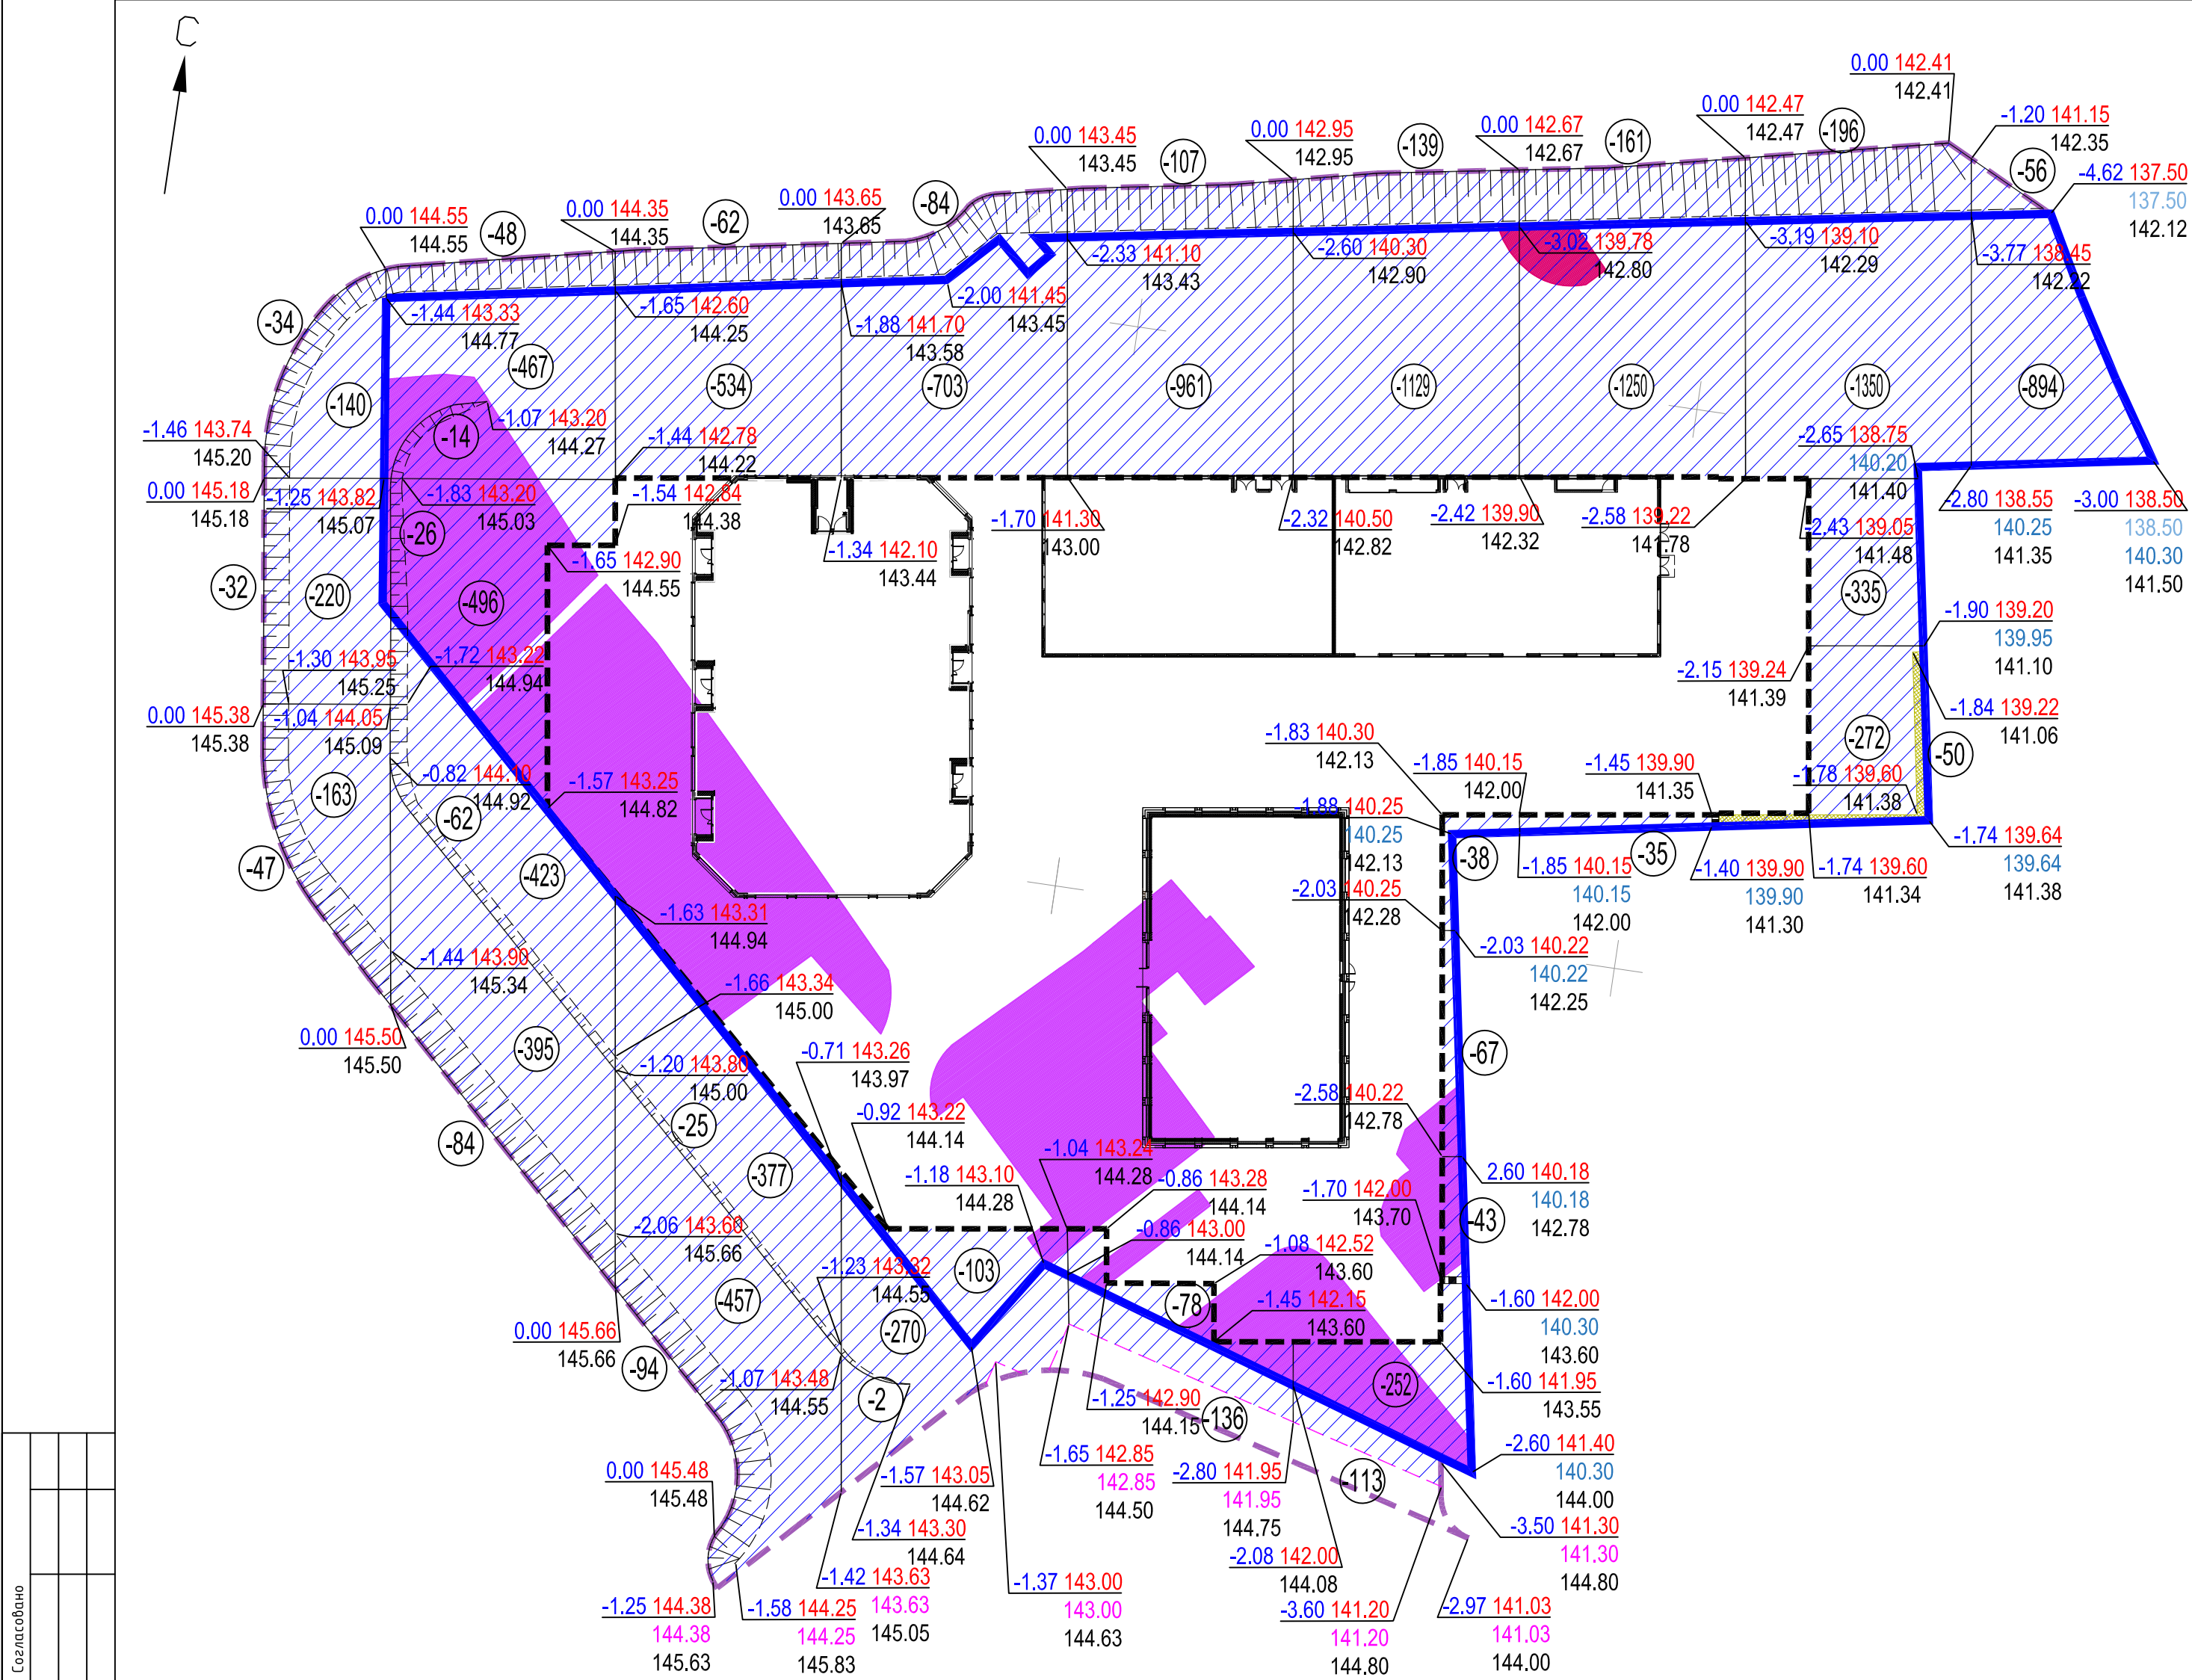

Баланс земляных масс

Наименование работ и объемов грунта	Количество, м3			
	ГПЗУ-1		Благоустройство	
	Насыпь (+)	Выемка (-)	Насыпь (+)	Выемка (-)
1. Планировка территории	-	9097	-	3927
2. Избыточный грунт от устройства:		65479		966
- корыта под одежду дорог, площадок, тротуаров		974		547
- фундаментов, подземных частей зданий и сооружений;		64165		-
- подземных инженерных коммуникаций		100		15
- корыта газона		240		404
3. Поправка грунта на уплотнение	-		-	
ИТОГО:	-	74576	-	4893
4. Избыток грунта	74576		4893	
5. Плодородный грунт				
а) используется для озеленения территории	770		424	
б) недостаток плодородного грунта		770		424
6. Итого перерабатываемого грунта	75346	75346	5317	5317

Примечание:
1. Данные для расчета избыточного грунта от устройства фундаментов и подвалов зданий и сооружений взяты с чертежей КР.
2. Объем плодородного грунта для озеленения территории дан с учетом объема растительного субстрата, используемого для посадки растительных насаждений на кровле автостоянки.
3. Согласно тому 01-386-23-ИЗИ "Технический отчет по результатам инженерно-экологических изысканий" загрязненные грунты расположены следующим образом:
- Пробная площадка 1 - грунтовые массивы территории, относящиеся к пробной площадке № 1 в слое 0,0- 0,2 м могут быть использованы в ходе строительных работ под отсыпки котлованов и выемок, на участках озеленения с подсыпкой слоя чистого грунта не менее 0,2 м. Объем данного грунта - 7м3.
- Пробная площадка 2 - грунтовые массивы территории, относящиеся к пробной площадке № 2 в слое 0,0- 0,2 м могут быть ограниченно использованы под отсыпки выемок и котлованов с перекрытием слоем чистого грунта не менее 0,5 м. Объем данного грунта - 345м3.

Условные обозначения

- граница участка в границах ГПЗУ-1
- граница территории благоустройства в границах ГПЗУ-2 и ГПЗУ-3
- контур подземного паркинга
- объем грунта
- рабочая отметка
- красная отметка (2-ая очередь)
- красная отметка (проект ДОО)
- красная отметка (1-ая очередь)
- красная отметка (Пр.проезд 8041)
- черная отметка
- участок выемки
- грунты, относящиеся к "умеренно опасной" категории загрязнения (пробная площадка 1)
- грунты, относящиеся к "опасной" категории загрязнения (пробная площадка 2)

насыпь (+)	-/-	-/-	-/-	-/-	-/-	-/-	-/-	-/-	-/-	Итого:	-/-
выемка (-)	-/636	-1003/-1012	-534/-1015	-806/-356	-1039/-243	-1529/-252	-1285/-161	-2007/-196	-894/-56		-9097/-3927

Примечание: над чертой - объем грунта в границах ГПЗУ-1
под чертой - объем грунта в границах благоустройства в границах ГПЗУ-2, ГПЗУ-3, ГПЗУ-4.

						360-ПД-ПЗУ1			
						«Строительство 2 очереди комплексной жилой застройки по адресу: г.Москва, ул.Нагатинская (ЖК 1й Нагатинский)», расположенный по адресу: г. Москва, ул. Нагатинская, д.1 (кадастровый номер земельного участка 77:05:0004001:2106).			
Изм.	Кол. уч.	Лист	№ док.	Подпись	Дата	Схема планировочной организации земельного участка	Стадия	Лист	Листов
Разработал		Соловьева					П	4	
ГАП		Варюхина							
						План земляных масс. М 1:500	ООО "Проект СПИЧ"		
ГМП		Малютин							