


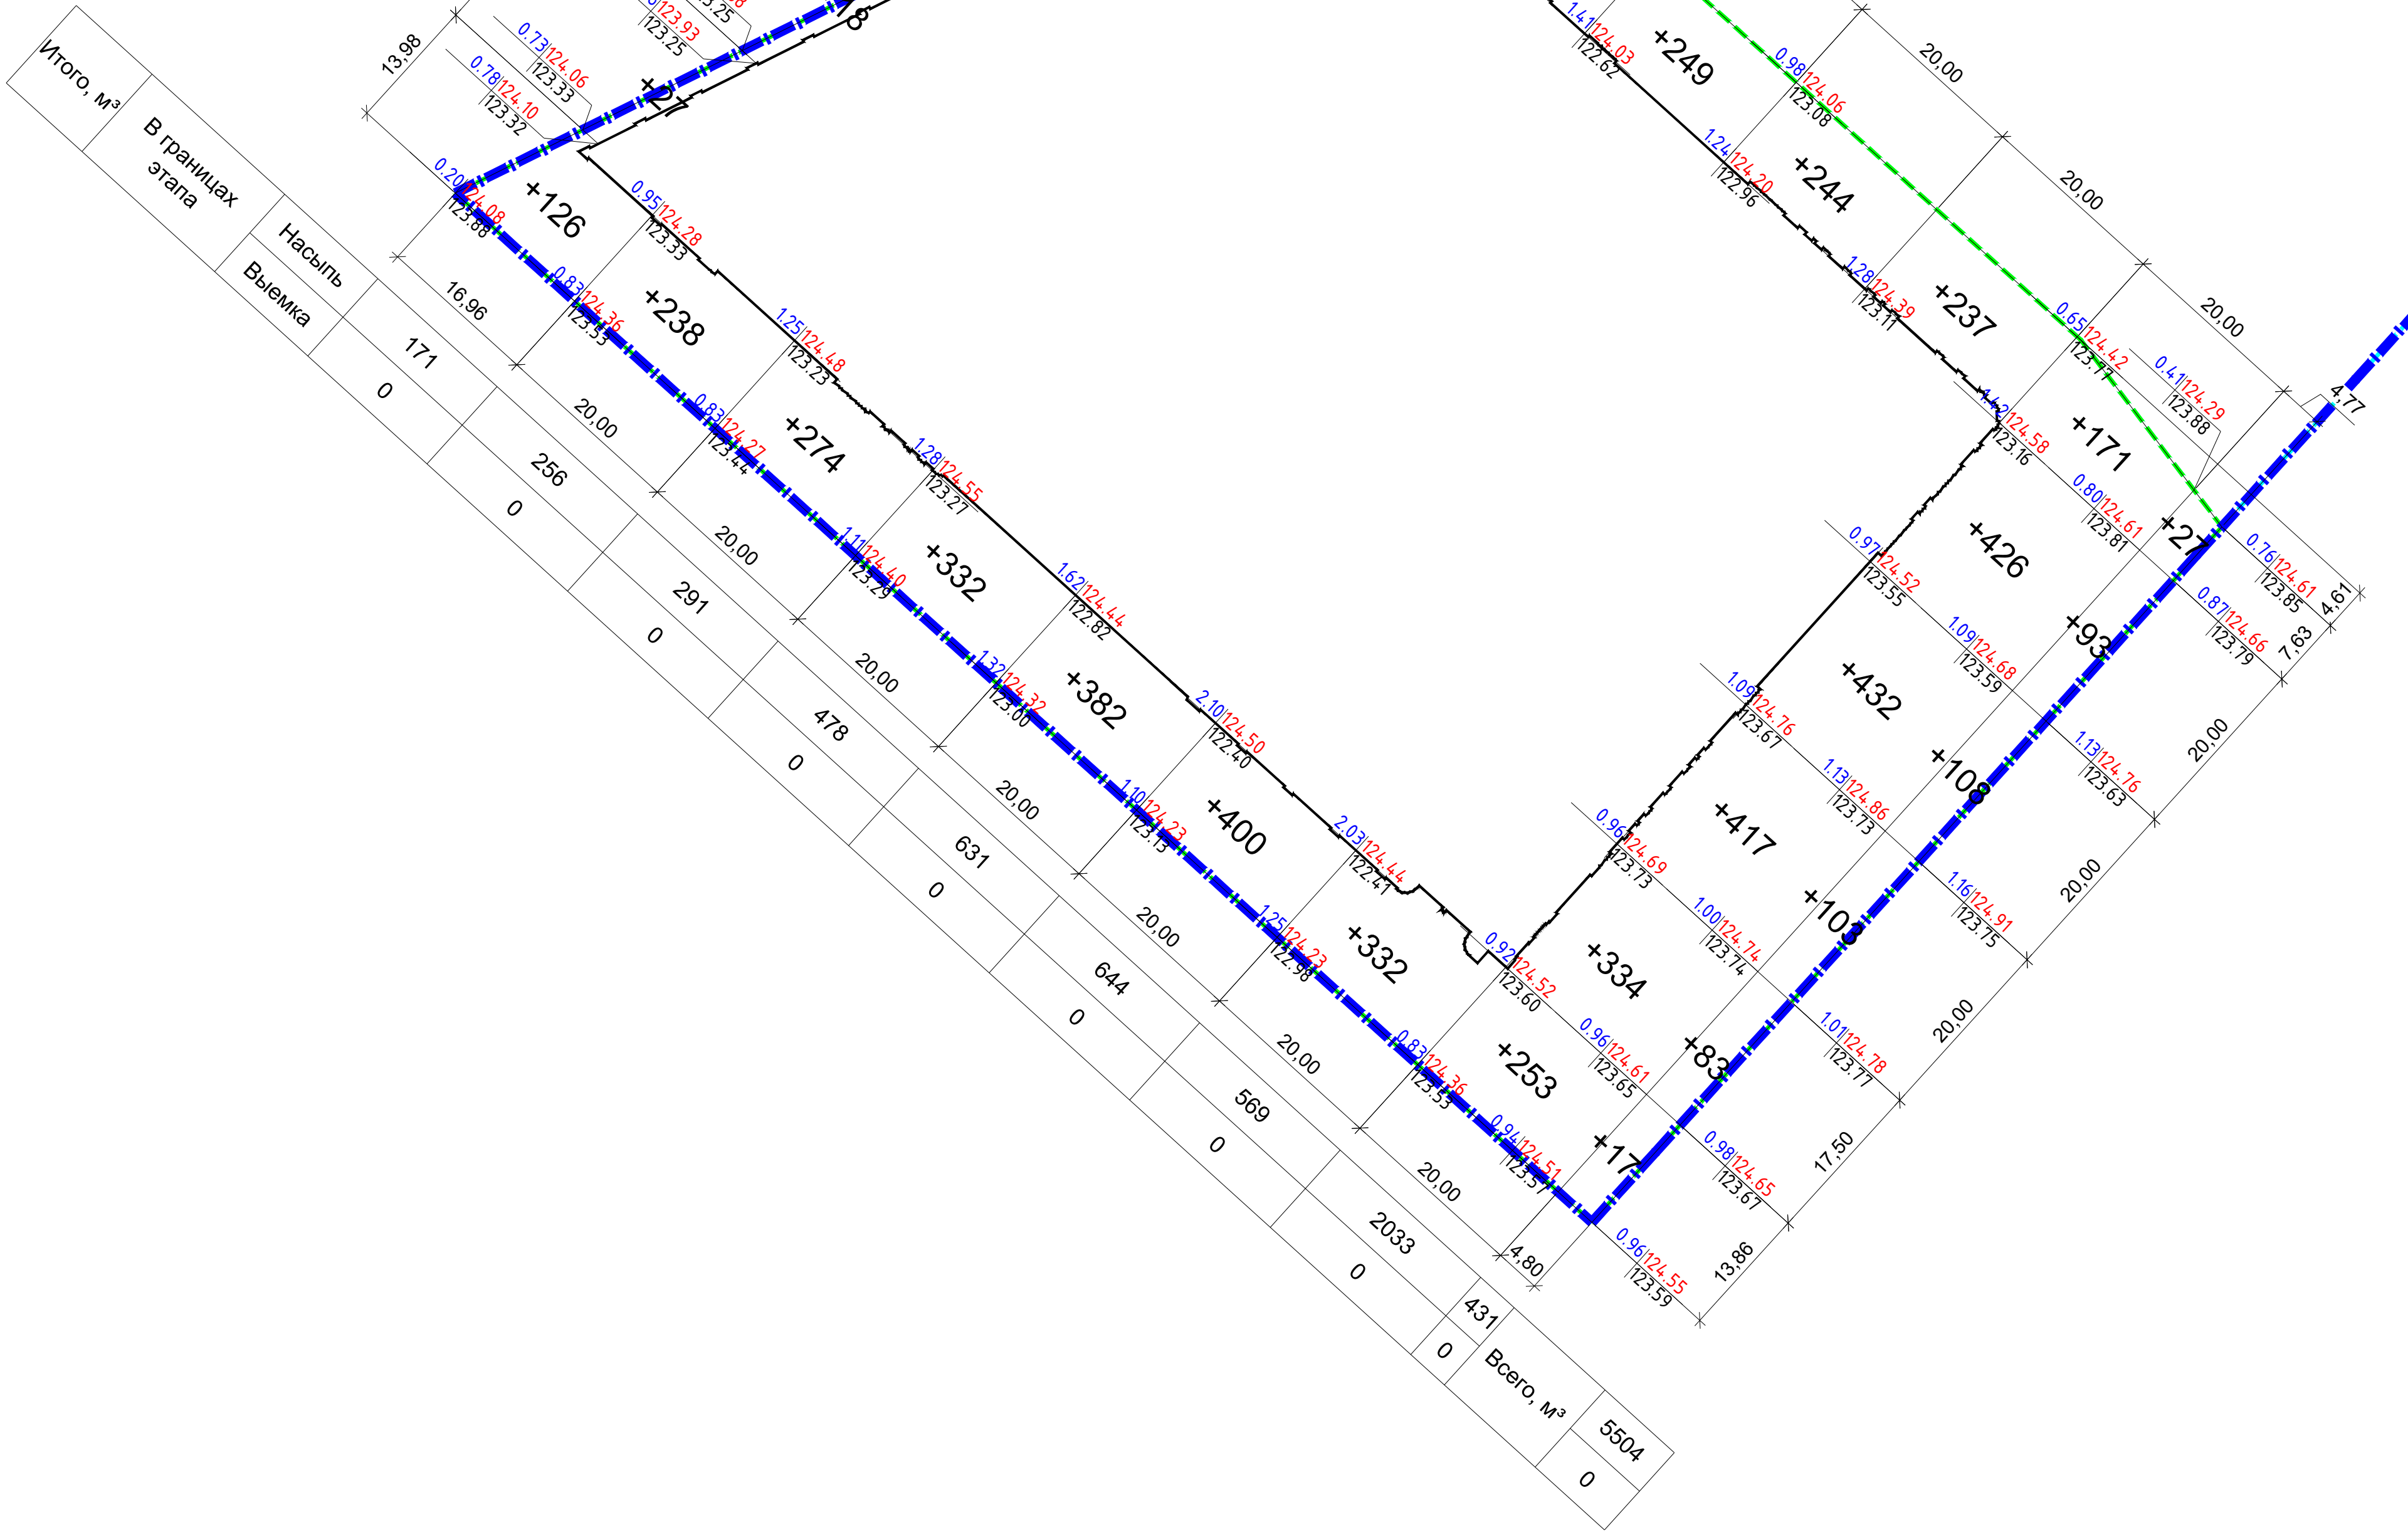

В результате комплексной оценки уровня загрязнения почв участка изысканий установлено, что все почвы и грунты на исследованной территории в слое от 0,0 до 7,0 м относятся к V классу опасности отходов для окружающей среды. Зона А, в пределах которой:

- почвы и грунты в районе пробных площадок 1,2,3 в слое 0,0-0,2 м относятся к "допустимой" категории загрязнения;
- грунты в интервале 0,2-7,0 м относятся к "допустимой" категории загрязнения.

Почвы-грунты со всей обследованной территории до глубины ведения работ 0,0-0,2 м и с 0,2-7,0 относятся к "допустимой" категории загрязнения, могут использоваться без ограничений. Согласно техническому отчету о результатах инженерно-экологических изысканий выполненному ООО "ЭТЭК" от 11.02.2025г.


 Граница земельного участка 77:05:00202005:34.12 (34.32)
 по ГПЗУ №РФ-77-4-59-3-14-2024-84-8-0 от 23.10.2024 г.
 Граница 2-го этапа строительства
 Граница 1-го этапа строительства
 Контур здания с учетом подземной части
 +192
 +0.05 124.25
 124.20
 Объем перемещаемого грунта, м.куб.
 Рабочая отметка Проекционная отметка
 Отметка по рельефу

						24.011-1-ПЗЧ		
						«Инскапартные» дана со встроено-пристроенными объектами и подземной автостоянкой. Этап по		
						эскизу		
						г. Москва, Вышнегорское муниципальное образование, Даниловское, д/п. Алмазовская, д/п. 23/71		
Изм.	Колуч	Лист	№ док.	Подп.	Дата		Стадия	Лист
Разработал	Ипатов			Ипатов	03.2025		П	4
ТИП	Боржковский				03.2025	План земельных масс М 1:500	ЭТАЛОН ПРОЕКТ	
Н. Контроль	Атлуханов				03.2025			